


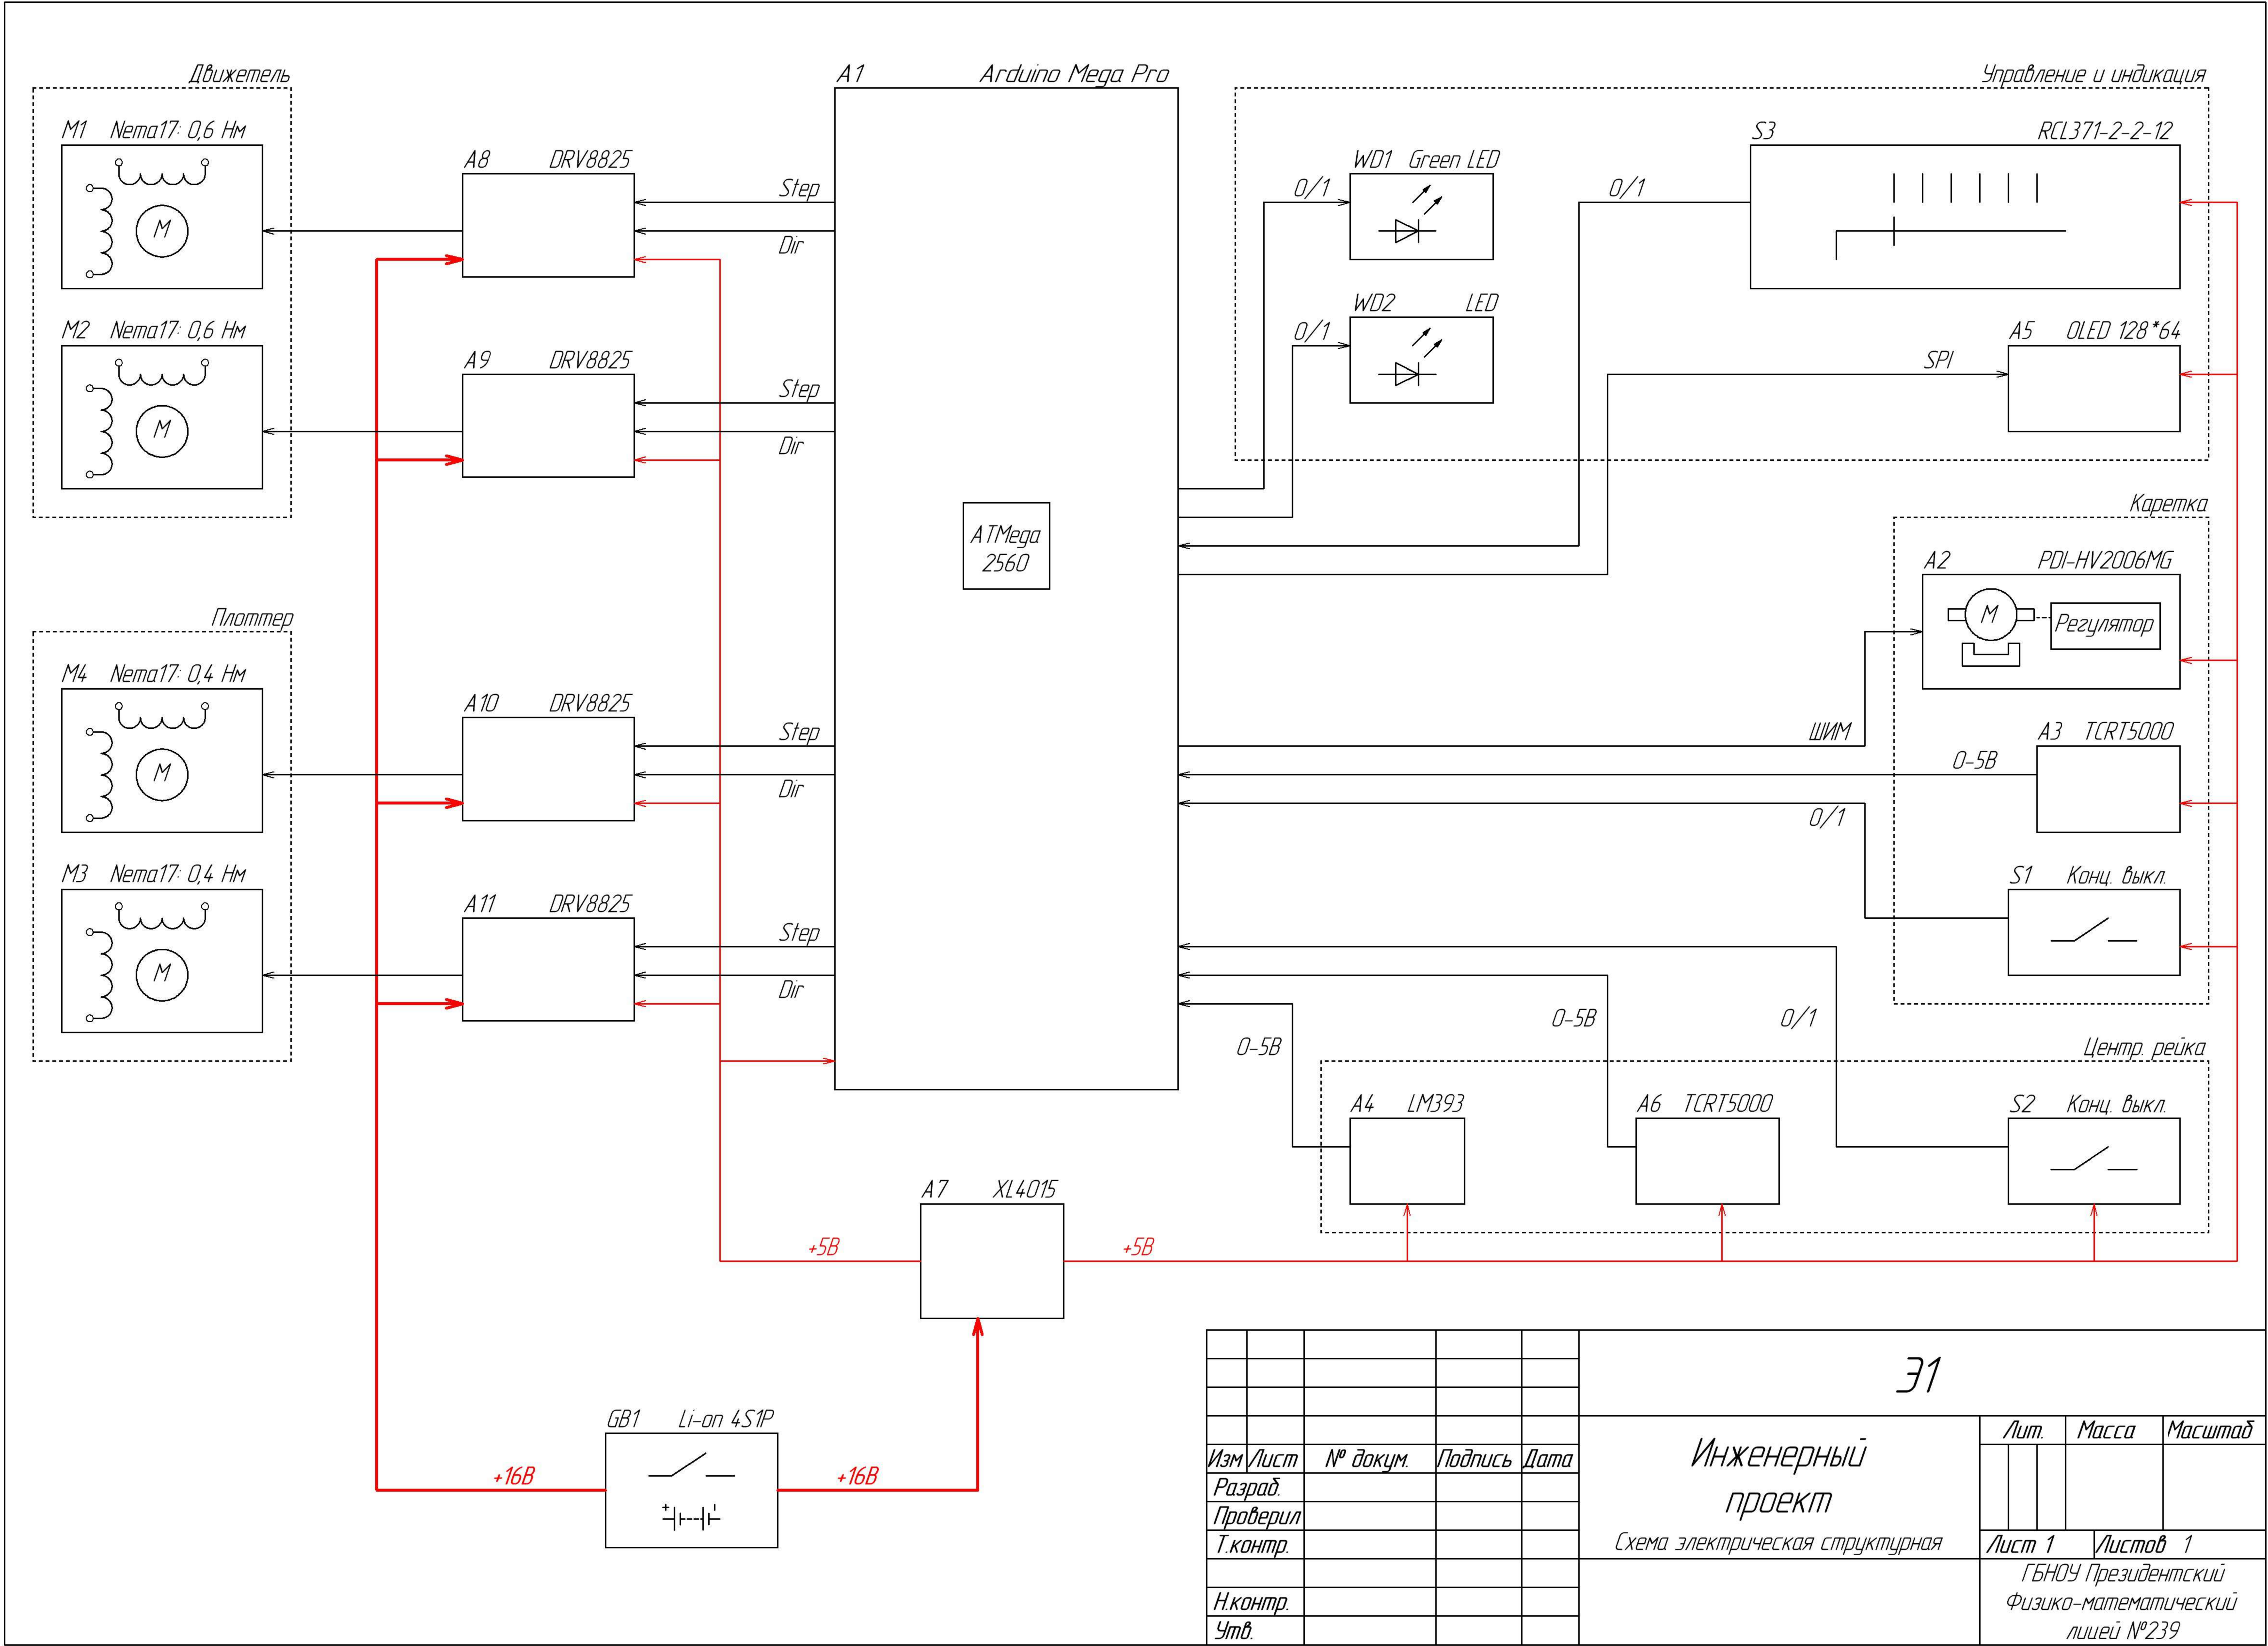

					31				
Изм	Лист	№ докум.	Подпись	Дата	Инженерный проект Схема электрическая структурная	Лит.		Масса	Масштаб
Разраб.									
Проверил									
Т.контр.						Лист 1		Листов 1	
Н.контр.						ГБНОУ Президентский Физико-математический лицей №239			
Утв.									