


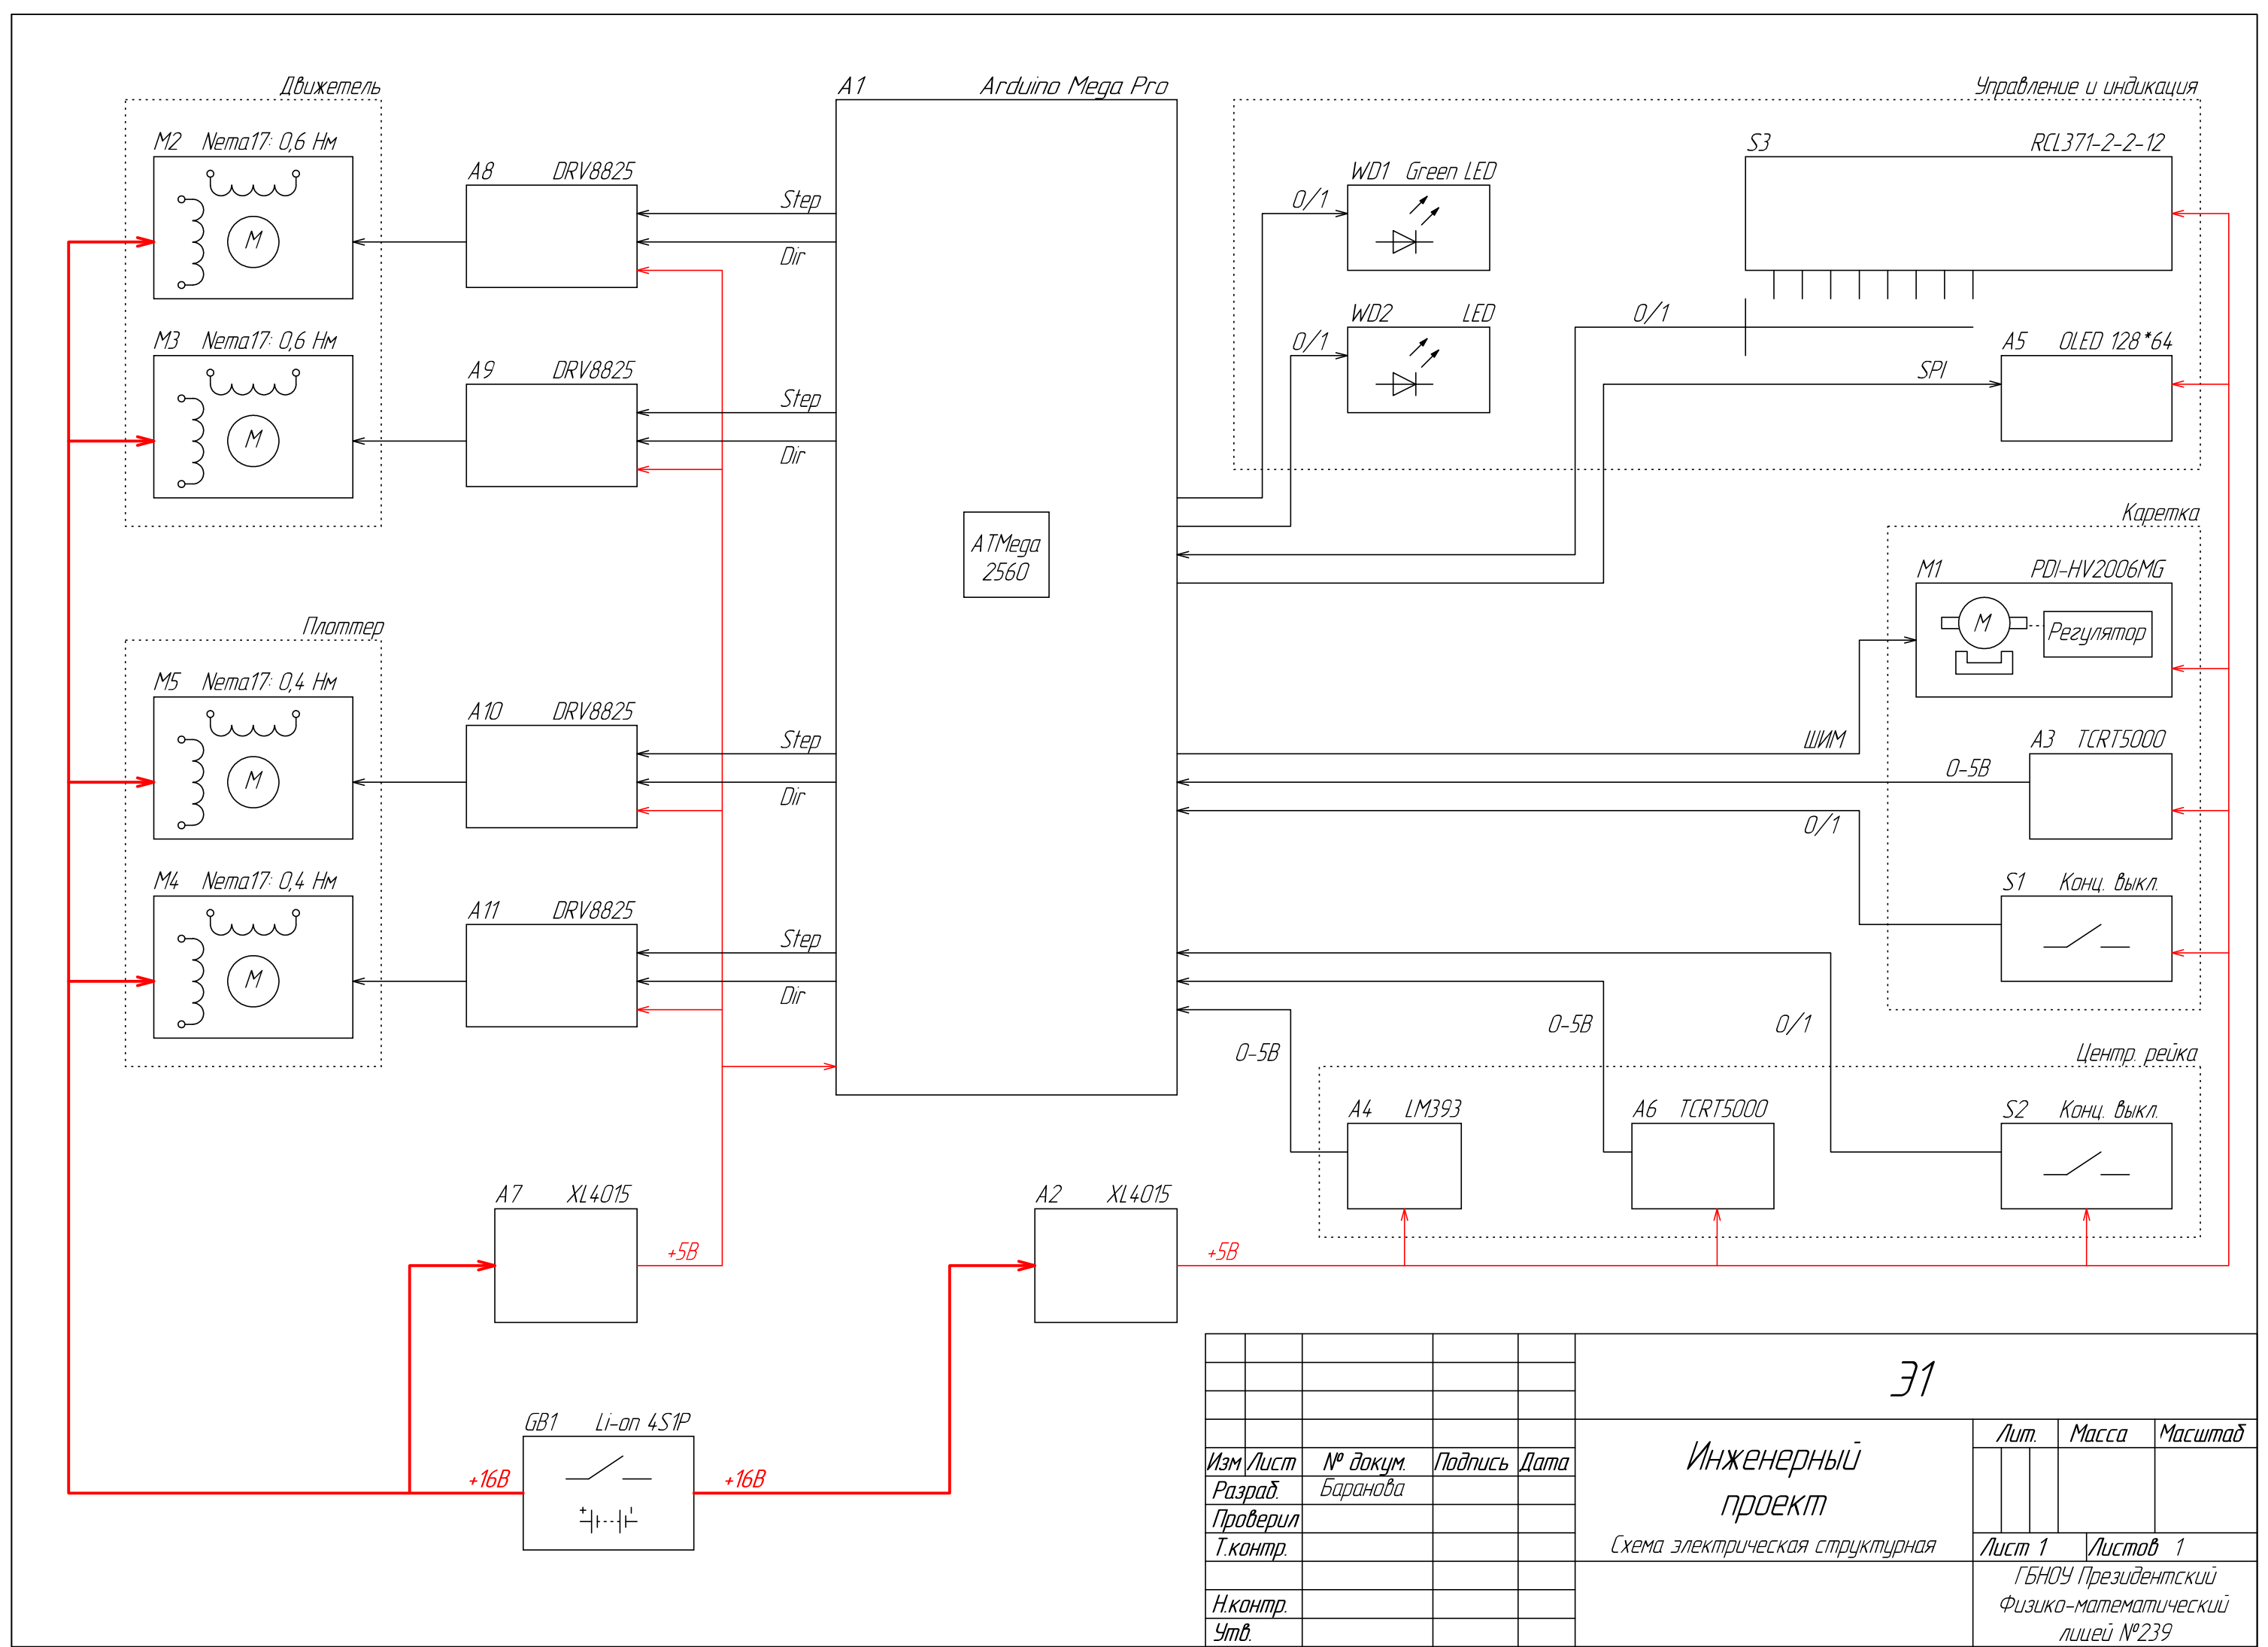

					31						
					Инженерный проект Схема электрическая структурная	Лит.			Масса	Масштаб	
Изм	Лист	№ докум.	Подпись	Дата							
Разраб.		Баранова									
Проверил											
Т.контр.											
Н.контр.											
Утв.						Лист 1		Листов 1			
						ГБОУ Президентский Физико-математический лицей №239					